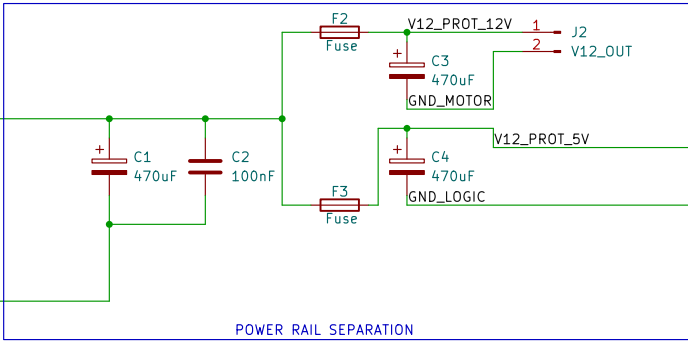
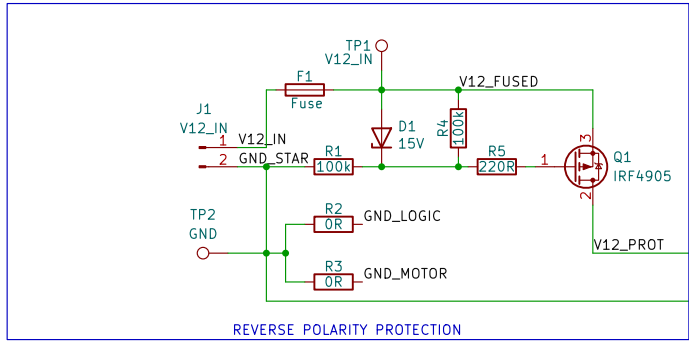


Sheet: /
File: card_issuance_power.kicad_sch

Title:


Size: A4

Date:

KiCad E.D.A. 9.0.7

Rev:

Id: 1/3

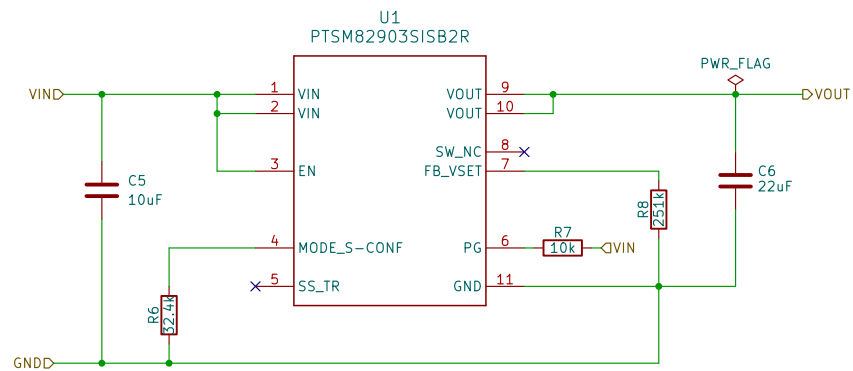

Sheet: /BUCK_3V3/
File: buck_3v3.kicad_sch

Title:


Size: A4

Date:

Rev:

KiCad E.D.A. 9.0.7

Id: 2/3

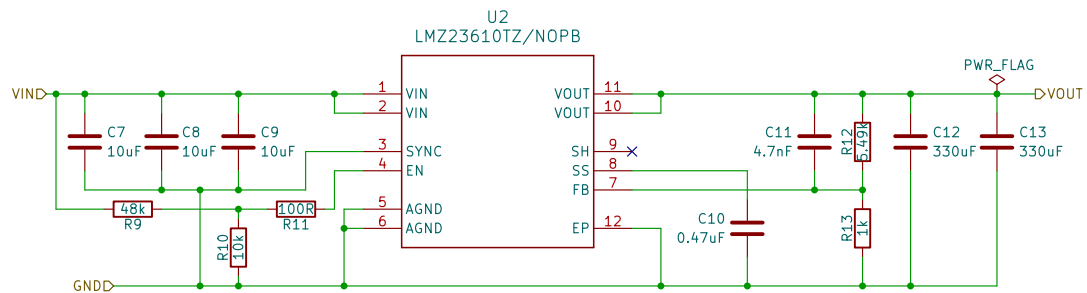

Sheet: /BUCK_5.1/
File: buck_5.1.kicad_sch

Title:

Size: A4
KiCad E.D.A. 9.0.7

Date:

Rev:
Id: 3/3